




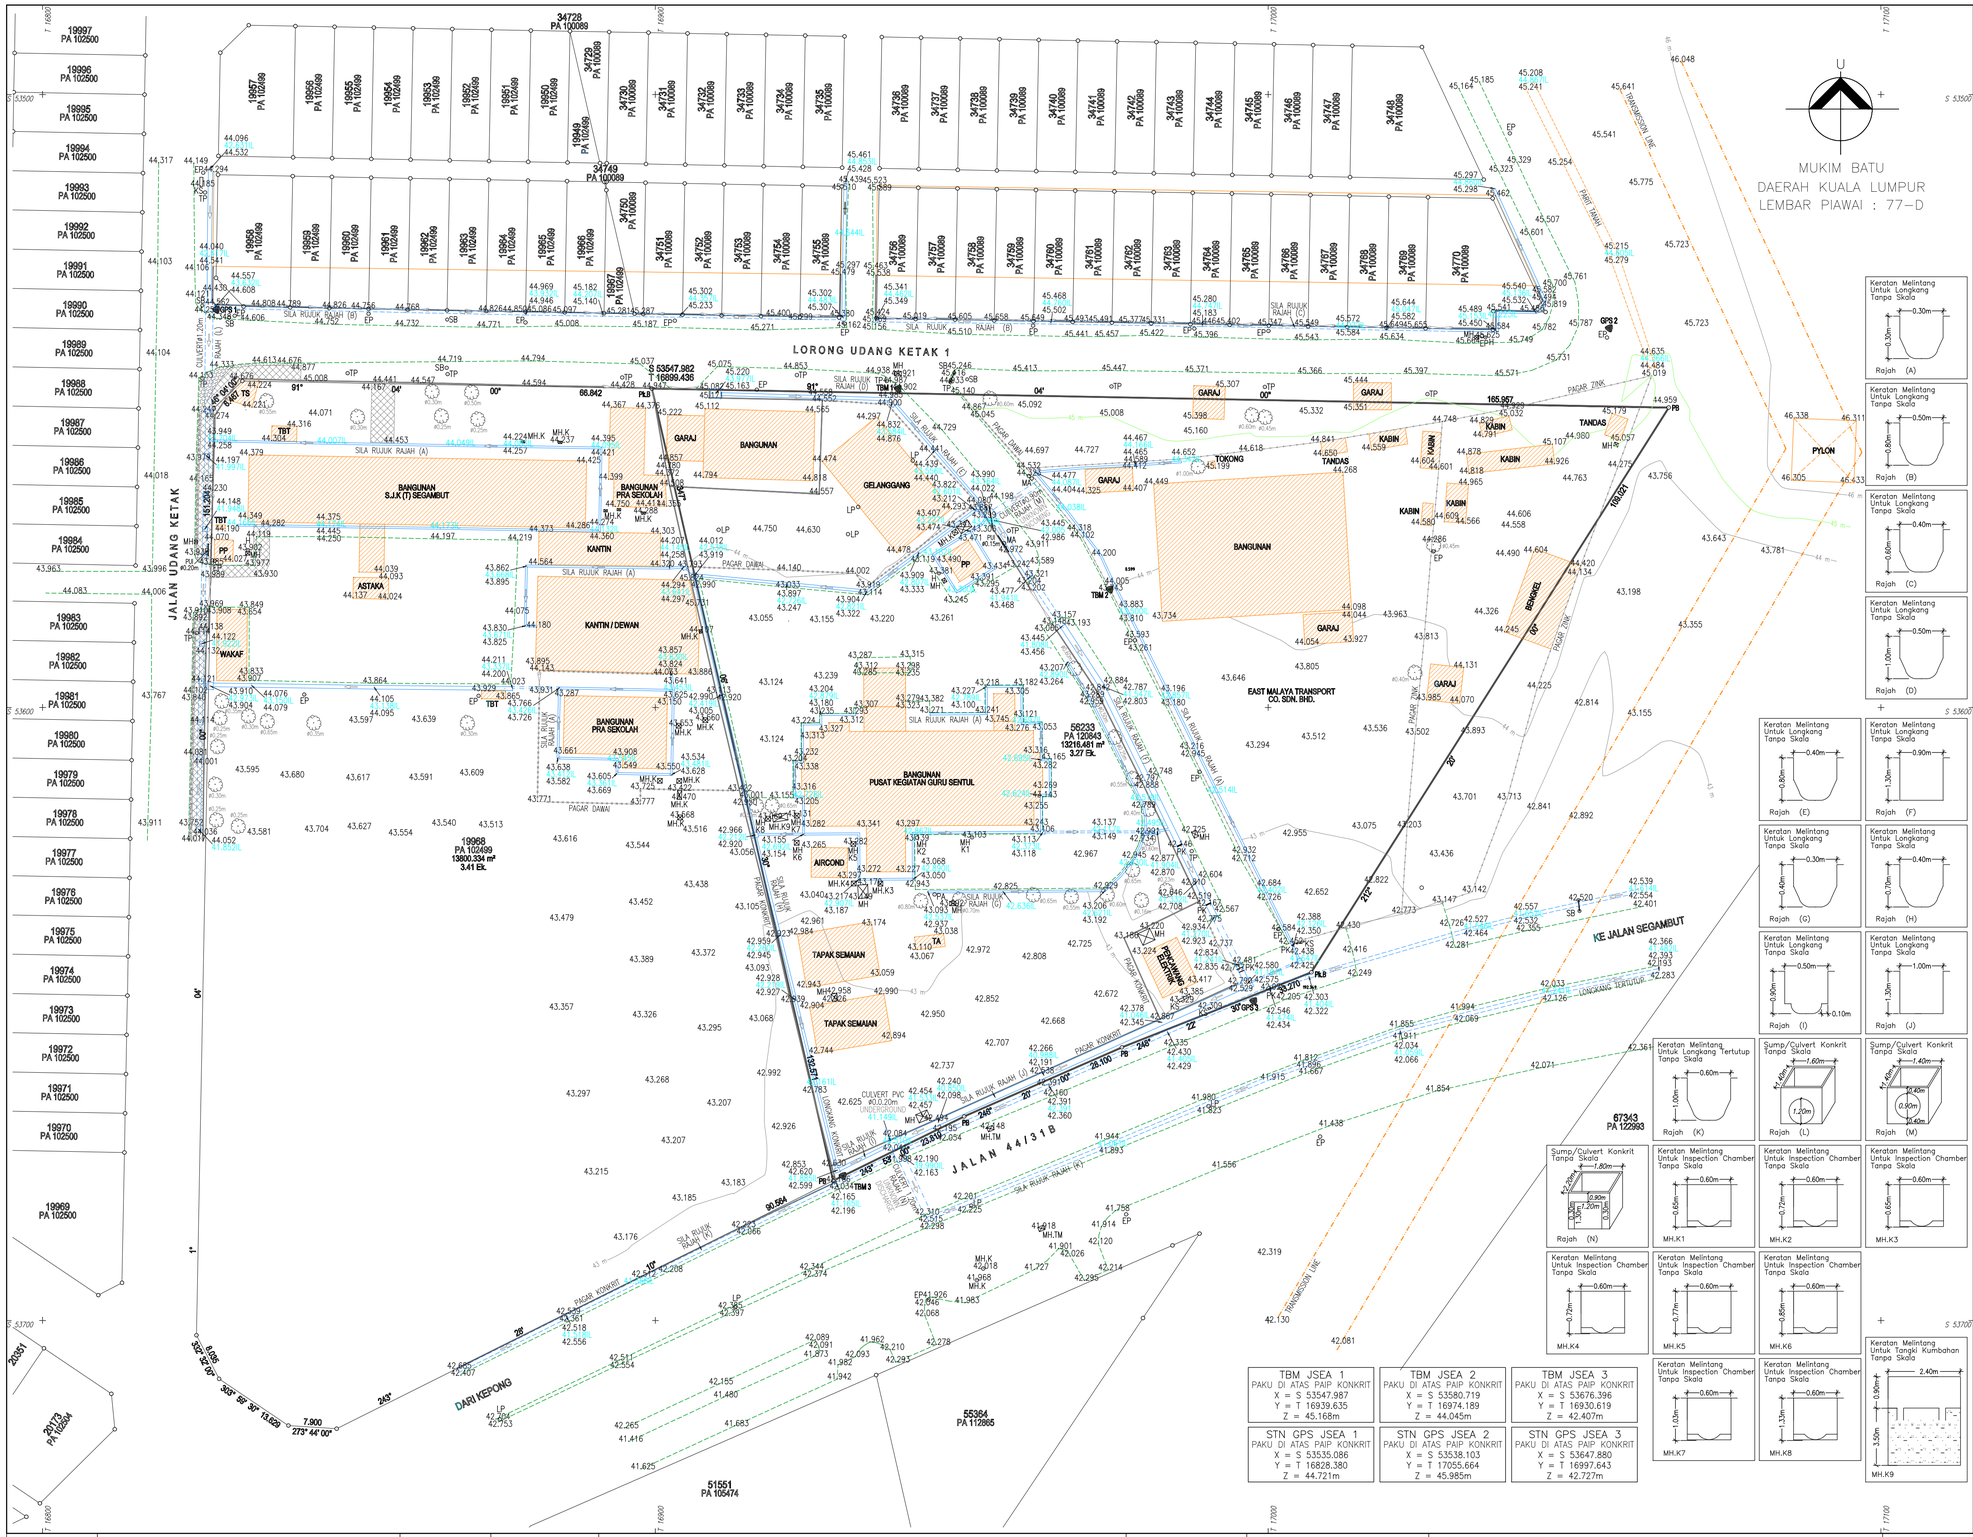


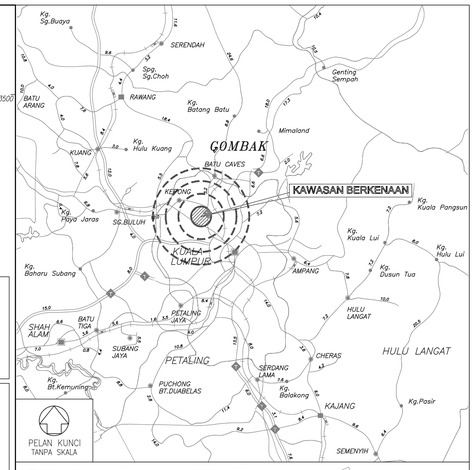

Keratan Melintang Untuk Longkang Tanpa Skala

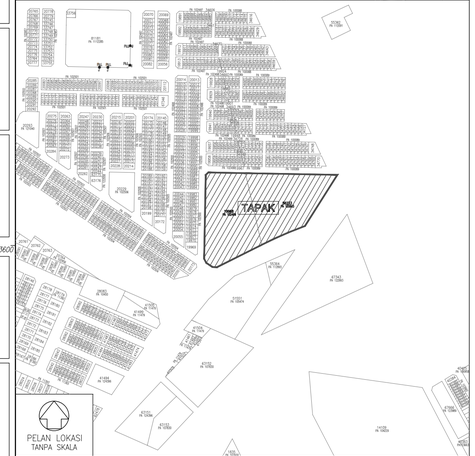



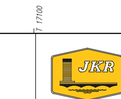

Sump/Culvert Konkrit Tanpa Skala

Keratan Melintang Untuk Inspection Chamber Tanpa Skala

Keratan Melintang Untuk Tangki Kumbahan Tanpa Skala

Keratan Melintang Untuk Longkang Tertutup Tanpa Skala

PETUNJUK:

Jalan	Tiang Bendera
Jalan Tanah	Tiang Elektrik
Lorong Pejalan Kaki	Tiang Telekom
Lorong Pejalan Kaki Berbumbung	Tiang Lampu
Tebing/Cerun	Pili Bomba
Pagar Dawai	Pili Air
Pagar Zink	Meter Air
Pintu Pagar	Papan Iklan/Tanda
Guard Rail	Marker TNB
Tembok Konkrit	Marker LV
Longkang Konkrit	Manhole
Culvert	Manhole Kumbahan
Sump Konkrit	Tempat Sampah
Parit Tanah	Pondok Pengawal
Pokok	Tempat Basuh Tangan
Kotak Suis	Batu Konkrit Lama
Lampu Limpah	Batu Konkrit Baru
Irigation Control Valve	Paip Baru
Peti Hos Bomba	Paip Lama
Paip Air	Pepaku Baru
Paip Kabel	Pepaku Lama

NOTA:

i) Semua ukuran dalam unit meter.

ii) Asas Koordinat GDM2000 Cassini–Soldner (MEI 2024)

iii) Kawalan mendatar di rujuk kepada Lot 81181 (PA 1112285).

iv) Ketinggian adalah berdasarkan kepada BM No. W 0101
Aras Laras = 43.072m
Di kiri Jalan Ipoh – Kuala Lumpur. Di tepi Bulatan Kepong.
Ketinggian adalah berdasarkan kepada BM No. W 61069
Aras Laras = 56.842m
Di kiri Jalan MRR2 menghala ke Kepong. Hadapan Stesen Pemindahan Sisa Pepejal Taman Beringin Kuala Lumpur.

v) Tarikh Mula Kerja Ukur : 02 Mei 2024

vi) Tarikh Siap Kerja Ukur : 16 Mei 2024

TBM JSEA 1	TBM JSEA 2	TBM JSEA 3
PAKU DI ATAS PAIP KONKRIT	PAKU DI ATAS PAIP KONKRIT	PAKU DI ATAS PAIP KONKRIT
X = S 53547.987	X = S 53580.719	X = S 53676.396
Y = T 16939.635	Y = T 16974.189	Y = T 16930.619
Z = 45.168m	Z = 44.045m	Z = 42.407m

STN GPS JSEA 1	STN GPS JSEA 2	STN GPS JSEA 3
PAKU DI ATAS PAIP KONKRIT	PAKU DI ATAS PAIP KONKRIT	PAKU DI ATAS PAIP KONKRIT
X = S 53535.086	X = S 53538.103	X = S 53647.880
Y = T 16828.380	Y = T 17055.664	Y = T 16997.643
Z = 44.721m	Z = 45.985m	Z = 42.727m

TARIKH	BUTIRAN	RUJUKAN	SKALA
			1 : 500
PINDAAN			

TAJUK PELAN :

PELAN UKURAN TOPOGRAFI DAN ARAS LARAS DI ATAS LOT 56233 DAN LOT 19968, MUKIM BATU, DAERAH KUALA LUMPUR, BAGI CADANGAN PEMBINAAN BAHARU PEJABAT PENDIDIKAN DAERAH SENTUL, WILAYAH PERSEKUTUAN KUALA LUMPUR.

SYIT PIAWAI	77–D
DI UKUR OLEH	CHE SAIDI
DILUKIS OLEH	WAN
DISEMAK OLEH	NOOR HAMIDI
TARIKH	17 MEI 2024
NO. PELAN	JSEA/KL/3848/2024–DETAIL_REV02

JURUKUR TANAH BERLESEN :

JURUKUR SAHARUDDIN EL–ASAS
(JURUKUR TANAH BERLESEN)
NO. 22–5, JALAN TASIK SELATAN 3, METRO CENTRE,
BANDAR TASIK SELATAN, 57000 KUALA LUMPUR.
TEL : 03–9057 6803, 03–9057 6804
FAX : 03–9054 6805.
email: jsealKl07@yahoo.com

NOOR HAMIDI BIN CHE DAN (LJT 440)
Jurukur Tanah Yang Di Lesen dibawah Akta 458 (Disemak 1991)

JABATAN KERJA RAYA MALAYSIA
CAWANGAN KEJURUTERAAN DAN INFRASTRUKTUR PENGANGKUTAN
Tingkat 8, Blok F
Ibu Pejabat JKR Malaysia
Jalan Sultan Salahuddin
50582 Kuala Lumpur

PEMBINAAN BAHARU PEJABAT PENDIDIKAN DAERAH SENTUL, WILAYAH PERSEKUTUAN KUALA LUMPUR.

BIL.

LUKISAN :